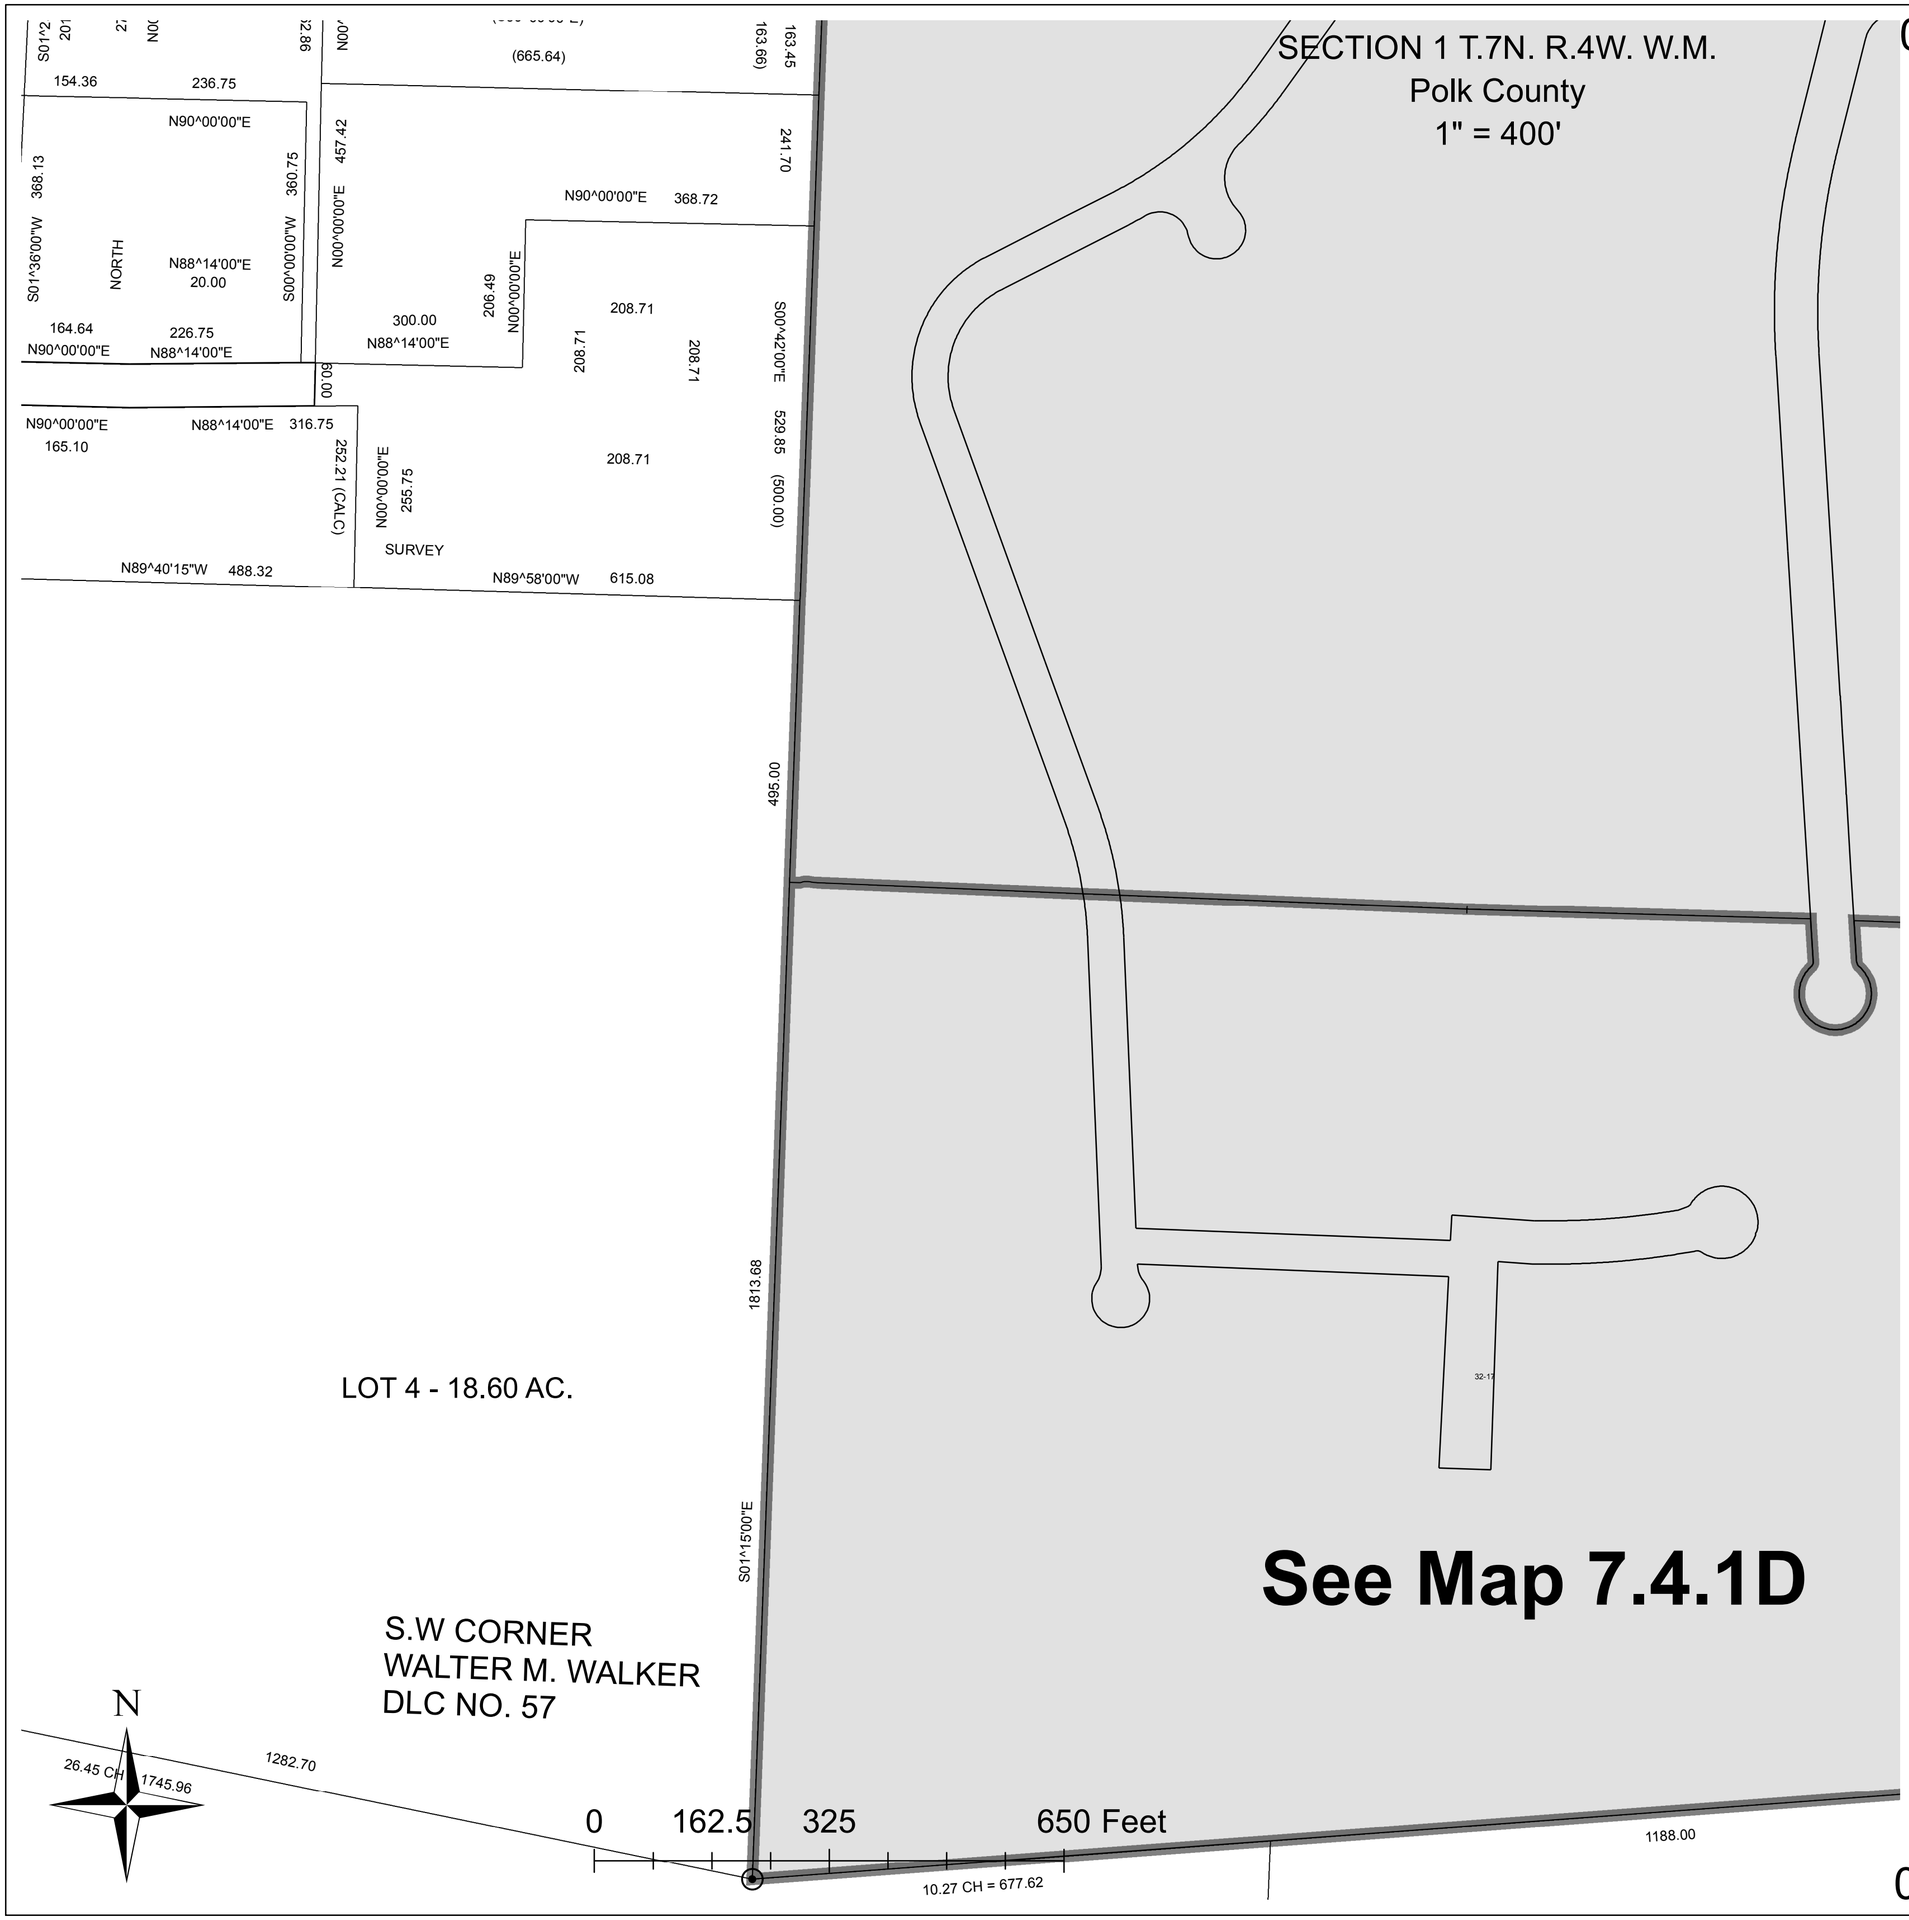


# 07 04 01

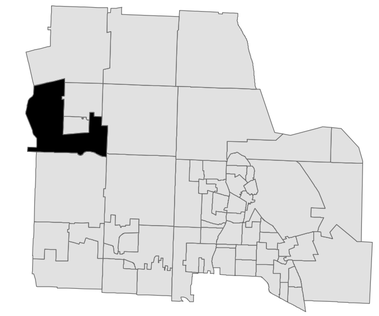

## Polk County Oregon

SECTION 1 T.7N. R.4W. W.M.

1" = 400'

| | | | | | | | |
|---|---|---|---|---|---|---|---|
| 36 | 31 | 32 | 33 | 34 | 35 | 36 | 31 |
| 1 | 6 | 5 | 4 | 3 | 2 | 1 | 6 |
| 12 | 7 | 8 | 9 | 10 | 11 | 12 | 7 |
| 13 | 18 | 17 | 16 | 15 | 14 | 13 | 18 |
| 24 | 19 | 20 | 21 | 22 | 23 | 24 | 19 |
| 25 | 30 | 29 | 28 | 27 | 26 | 25 | 30 |
| 36 | 31 | 32 | 33 | 34 | 35 | 36 | 31 |
| 1 | 6 | 5 | 4 | 3 | 2 | 1 | 6 |

FOR ADDITIONAL MAPS VISIT OUR WEBSITE AT
www.co.polk.or.us

| | | | |
|---|---|---|---|
| BB | BA | AB | AA |
| BC | BD | AC | AD |
| CB | CA | DB | DA |
| CC | CD | DC | DD |

Cancelled Taxlots For: 07 04 01

100, 200, 800, 1000 THRU 1800

PLOT DATE: 2010-03-11

*FOR ASSESSMENT PURPOSES ONLY - DO NOT RELY ON FOR OTHER USE*

*Map areas delineated by either gray shading or a cross-hatched pattern are for reference only and may not indicate the most current property boundaries. Please consult the appropriate map for the most current information.*

07 04 01